grafici di cui al Decreto n.15/32/98 del 28/05/1999. Legge 219/81 e succ.ve

PIANTA PIANO SEMINTERRATO E FONDAZIONI

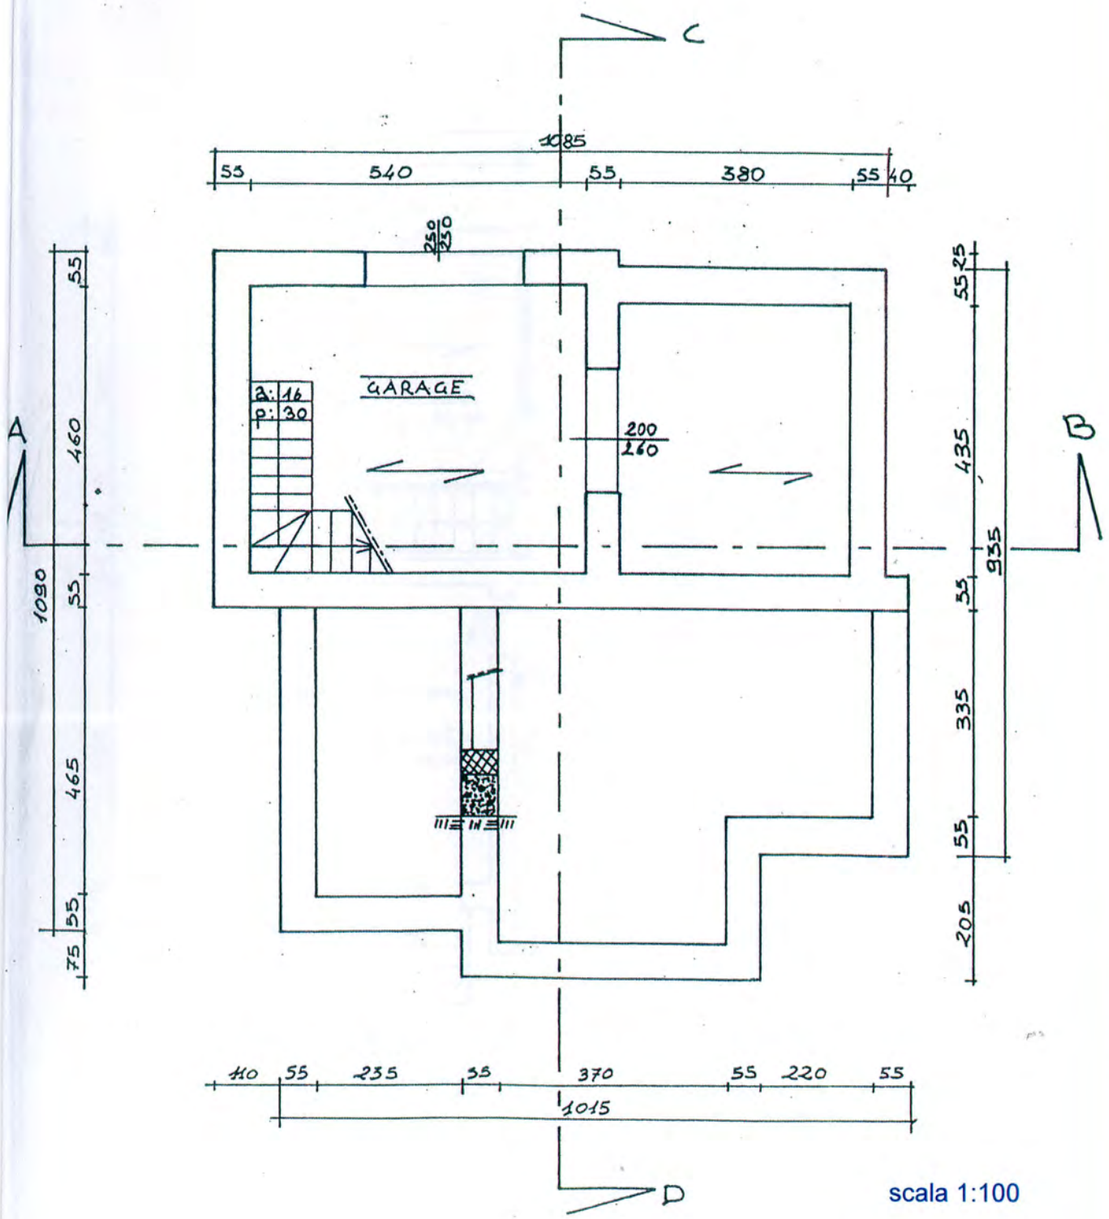

scala 1:100

grafici Progetto a Sanatoria

PIANO SEMINTERRATO

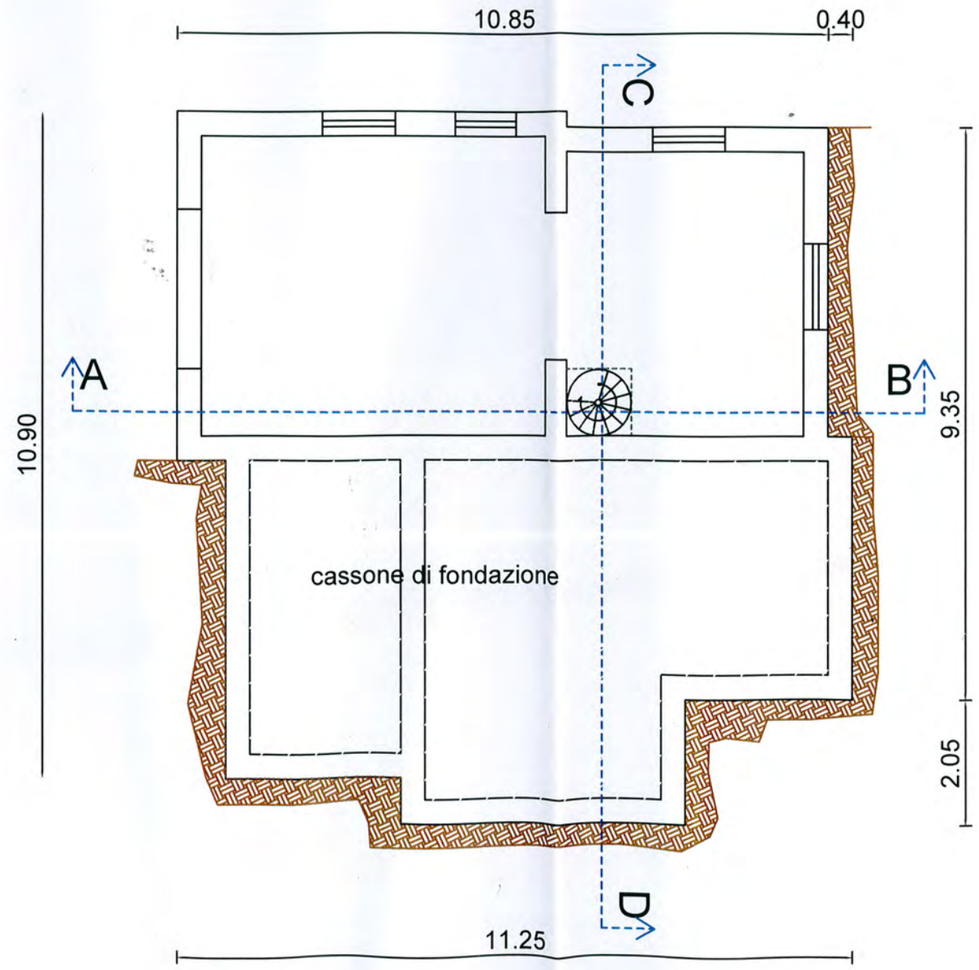

grafici di cui al Decreto n.15/32/98 del 28/05/1999. Legge 219/81 e succ.ve

PIANTA PIANO RIALZATO

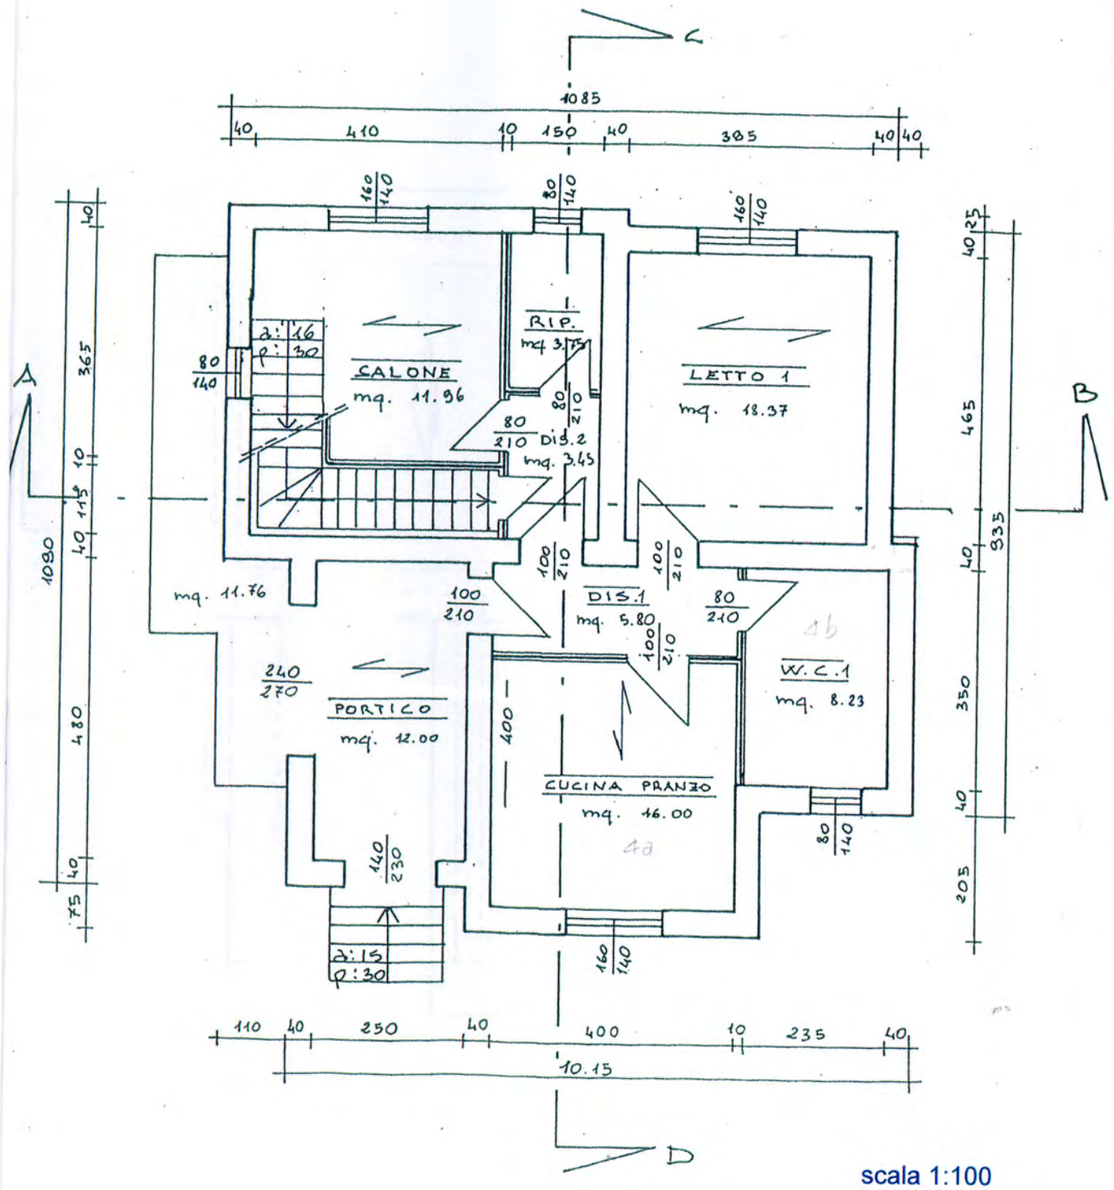

scala 1:100

grafici Progetto a Sanatoria

PIANO RIALZATO

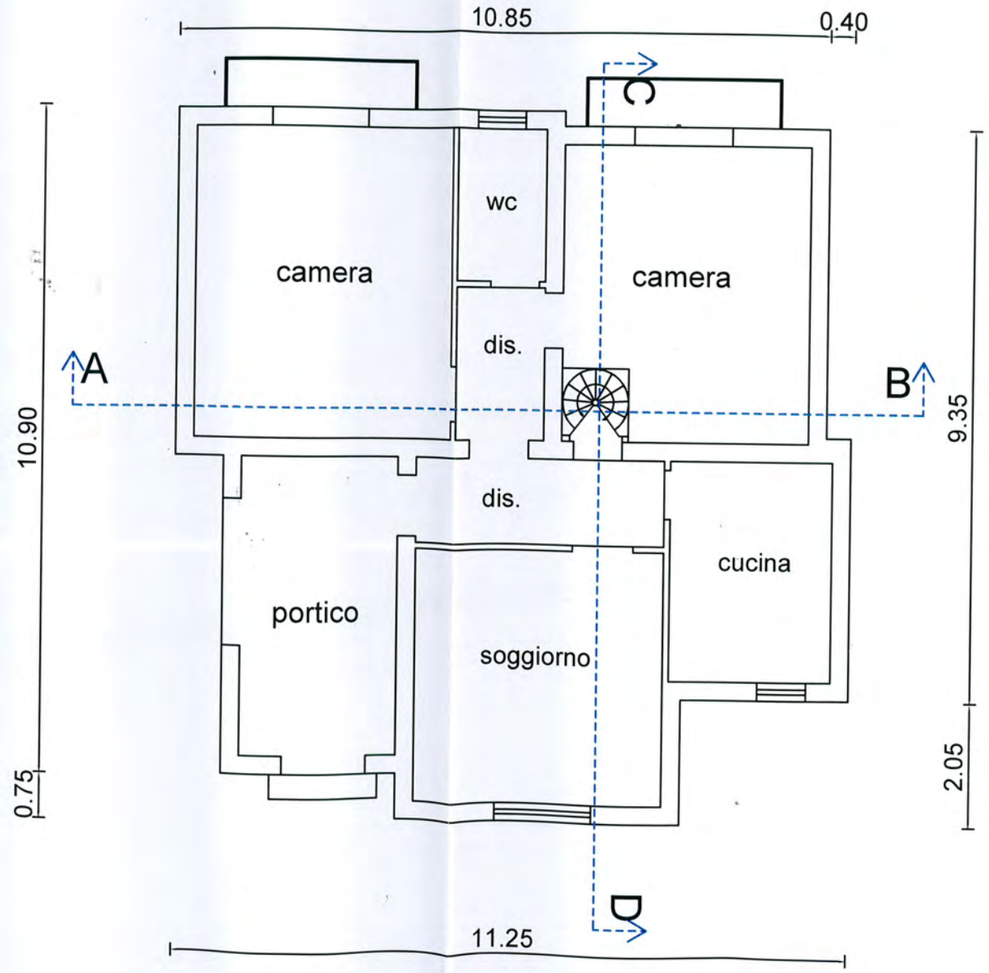

scala 1:100

grafici di cui al Decreto n.15/32/98 del 28/05/1999. Legge 219/81 e succ.ve

PIANTA COPERTURA

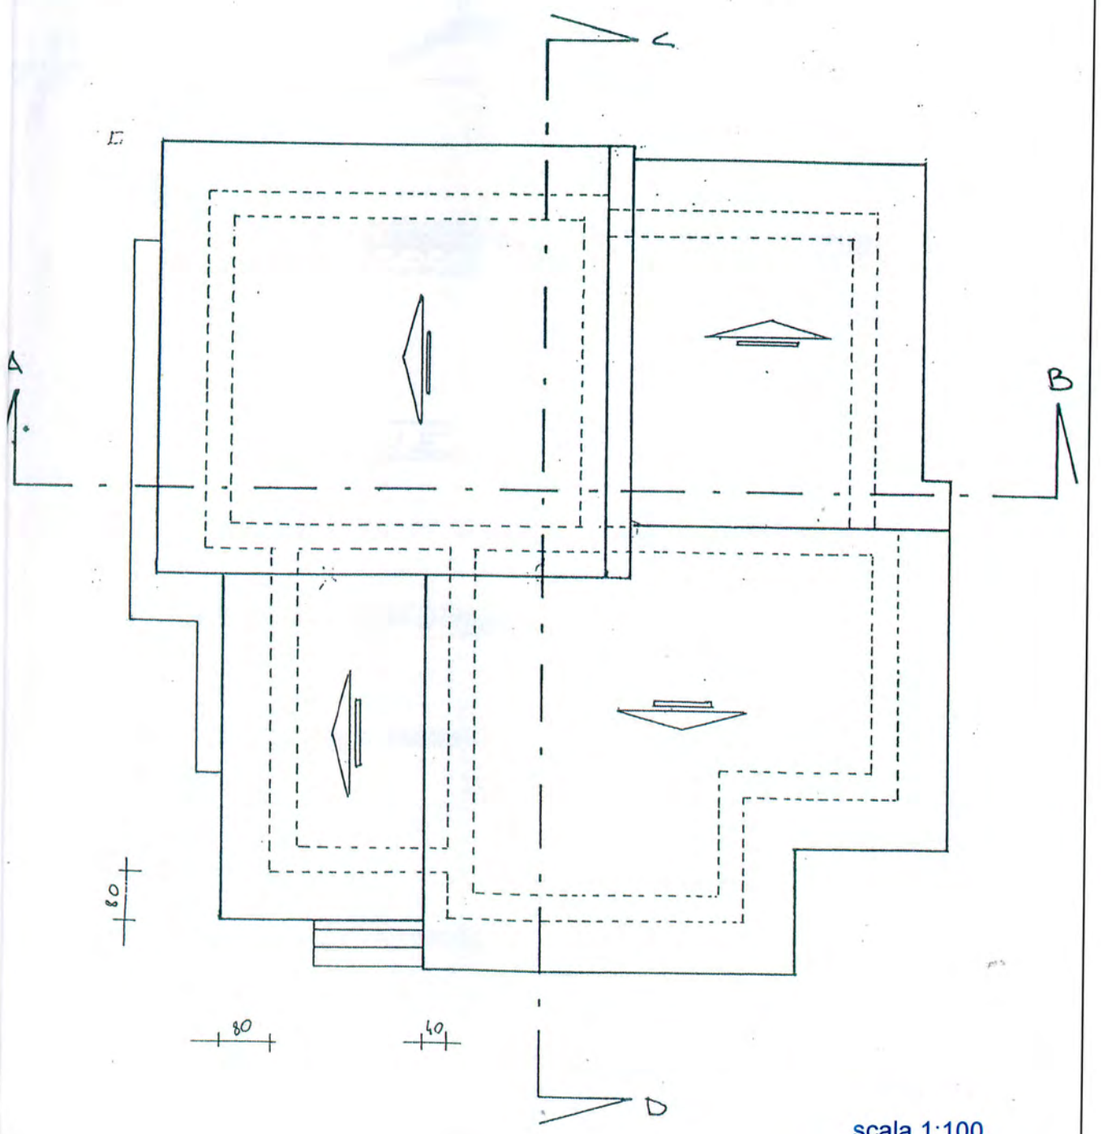

scala 1:100

grafici Progetto a Sanatoria

PIANTA COPERTURA

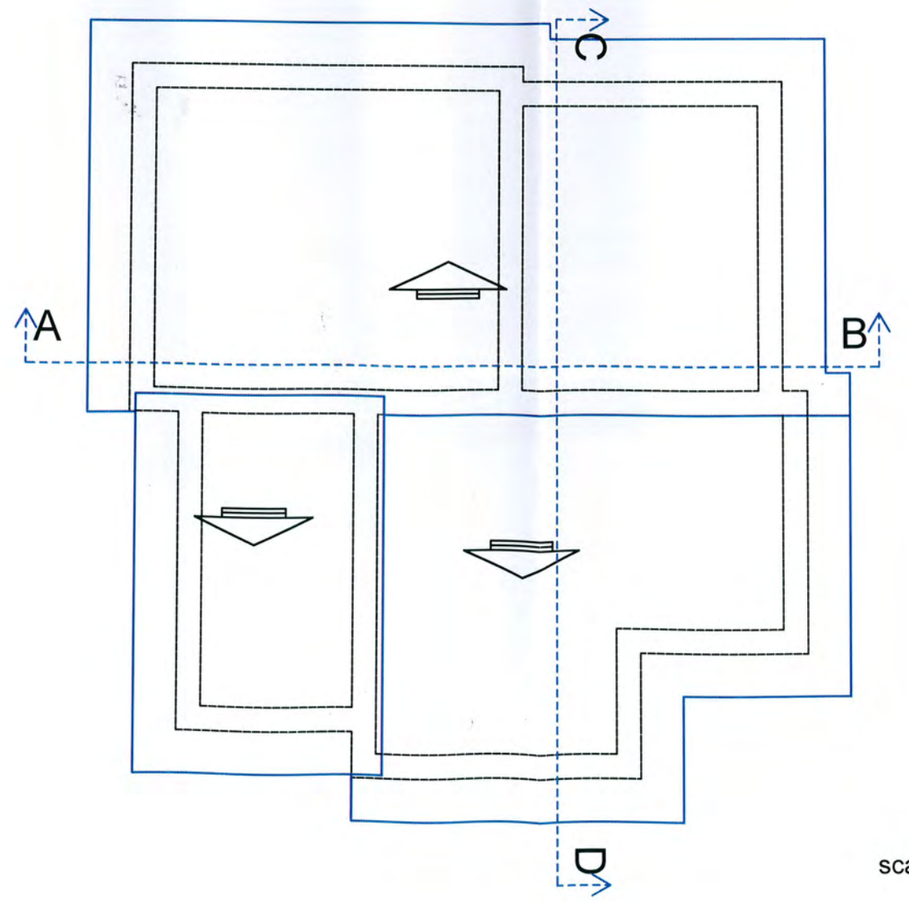

scala 1:100

grafici di cui al Decreto n.15/32/98 del 28/05/1999.
Legge 219/81 e succ.ve

SEZIONE A - B

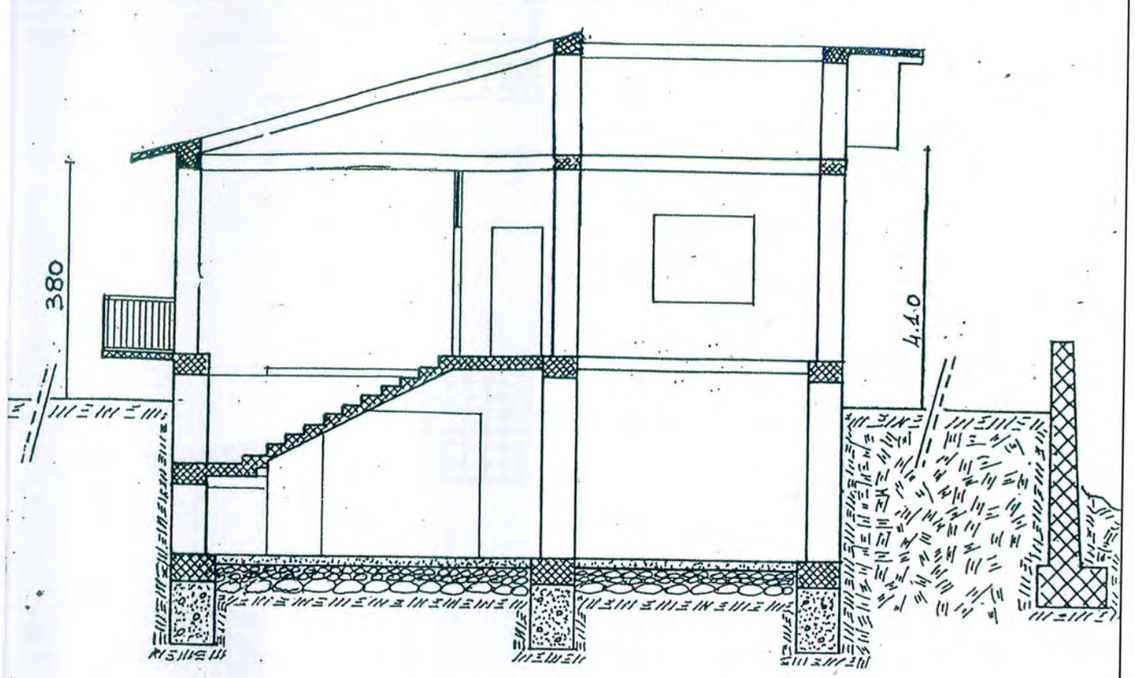

SEZIONE C - D

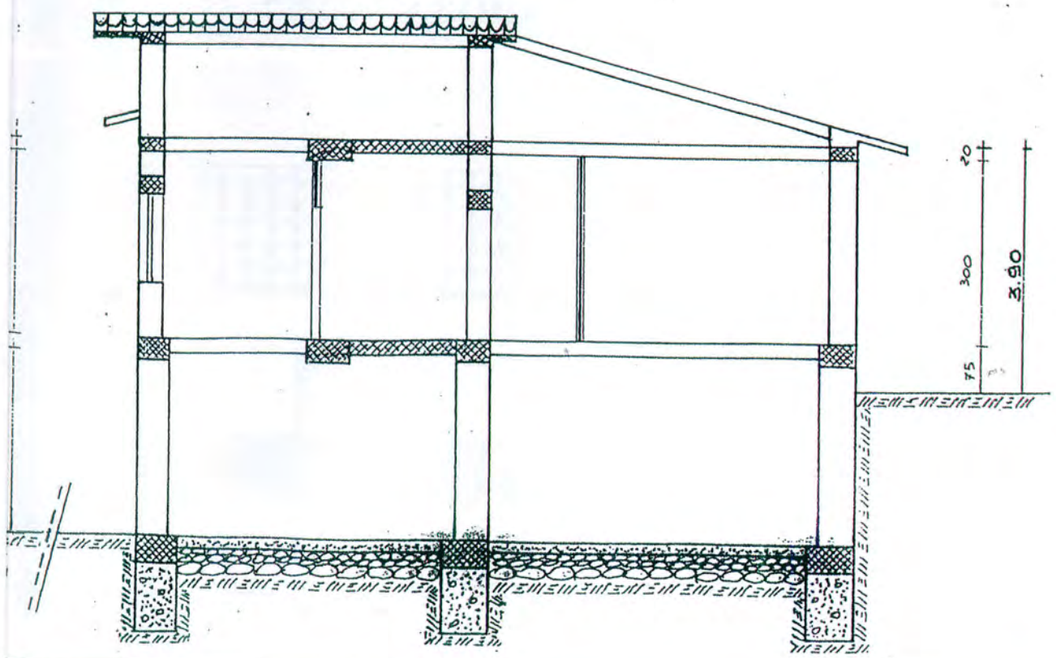

grafici Progetto a Sanatoria

SEZIONE AB

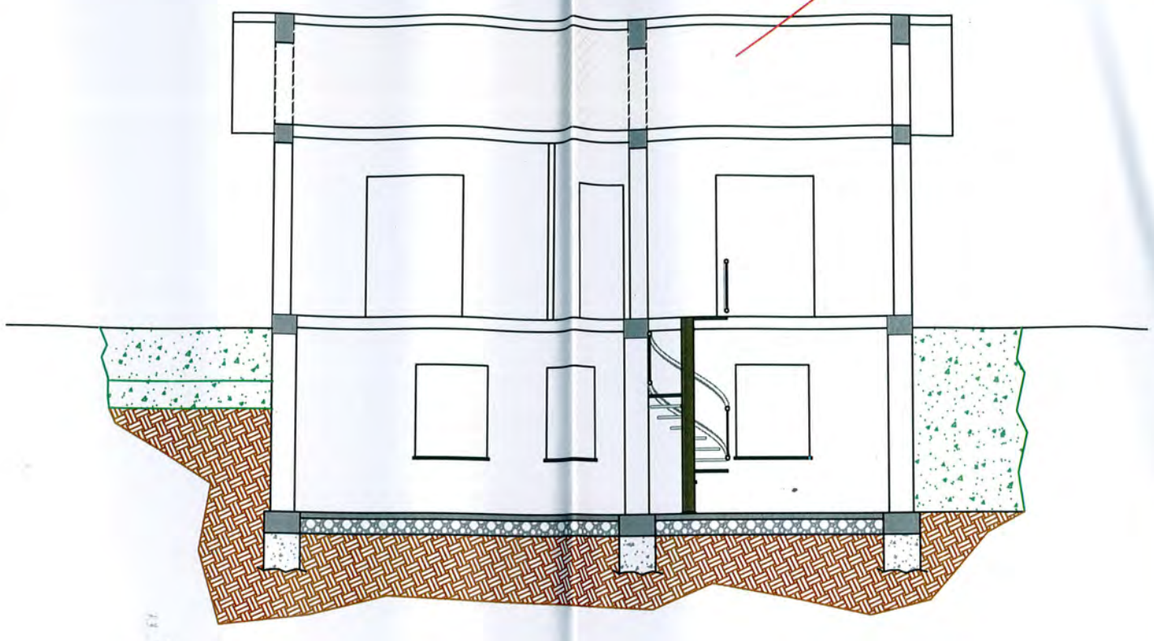

SEZIONE CD

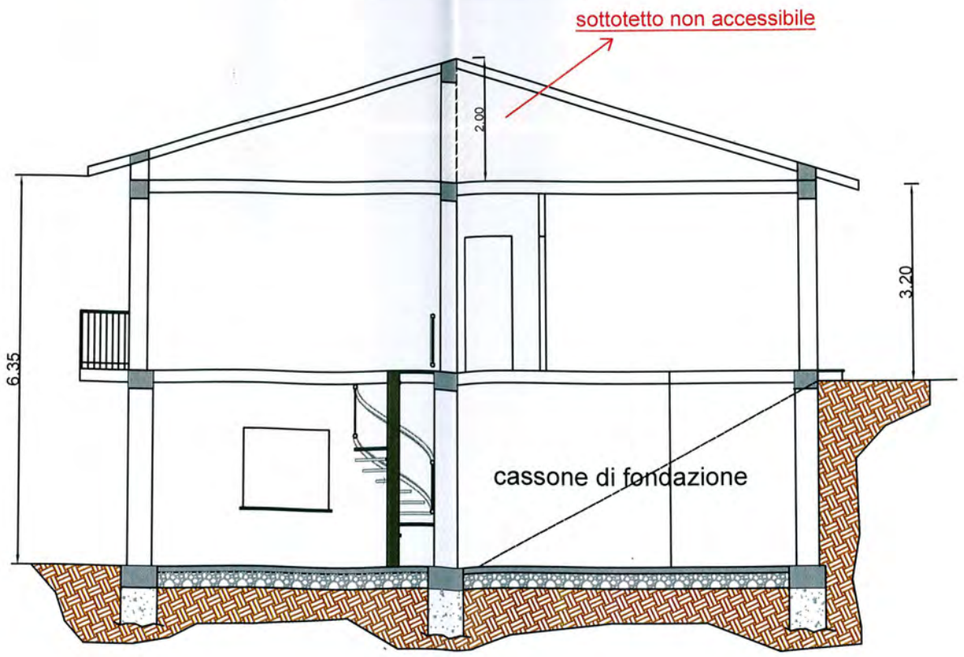

scala 1:100

rafici di cui al Decreto n.15/32/98 del 28/05/1999. Legge 219/81 e succ.ve

PROSPETTO PRINCIPALE

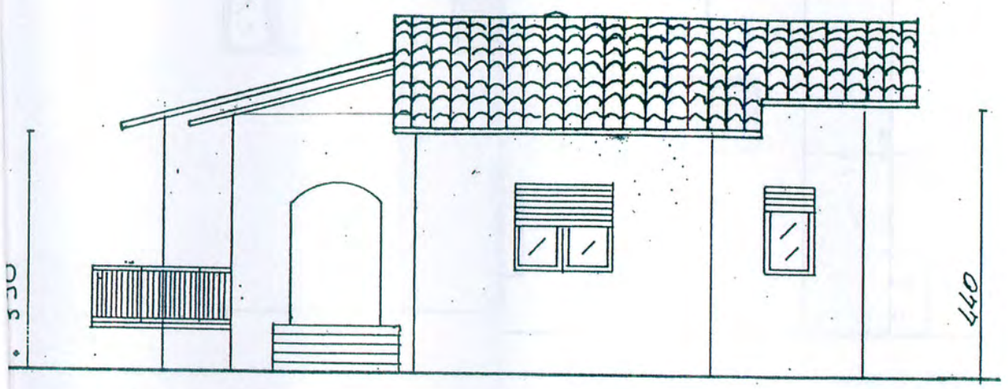

PROSPETTO LATERALE Sx

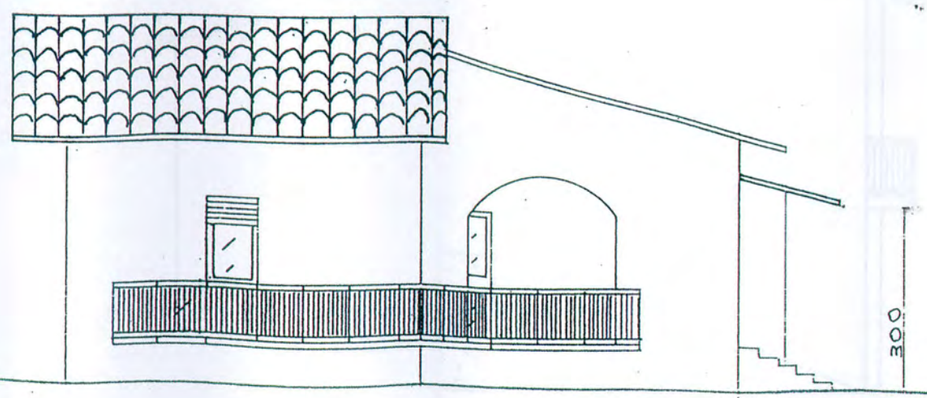

scala 1:100

grafici Progetto a Sanatoria

calcolo Hm = (3.80+3.85)/2 = mt 3.825

PROSPETTO FRONTALE

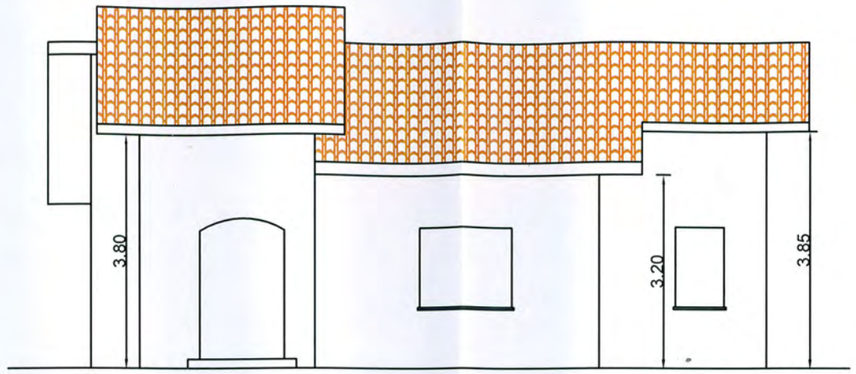

PROSPETTO LATERALE SX

calcolo Hm = (6.25+3.80)/2 = mt 5.025

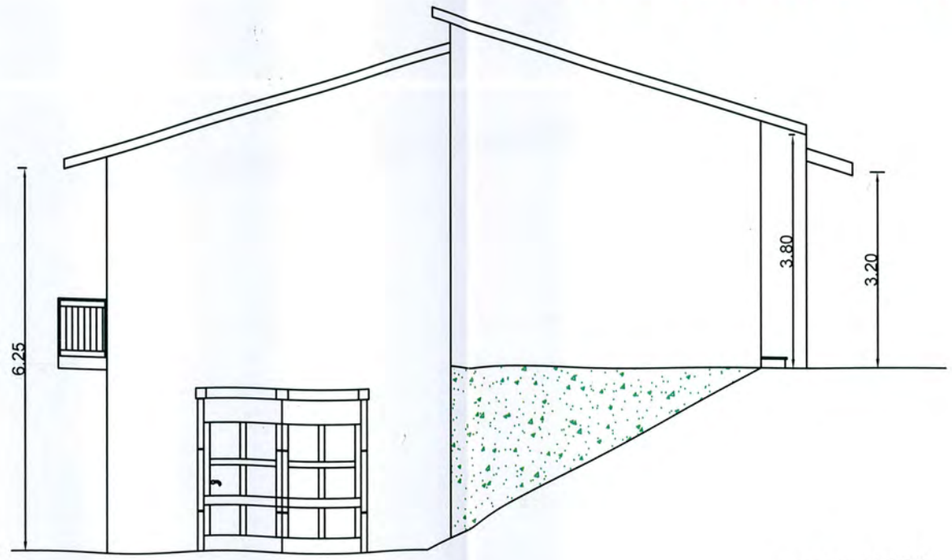

scala 1:100

grafici di cui al Decreto n.15/32/98 del 28/05/1999. Legge 219/81 e succ.ve

PROSPETTO POSTERIOR

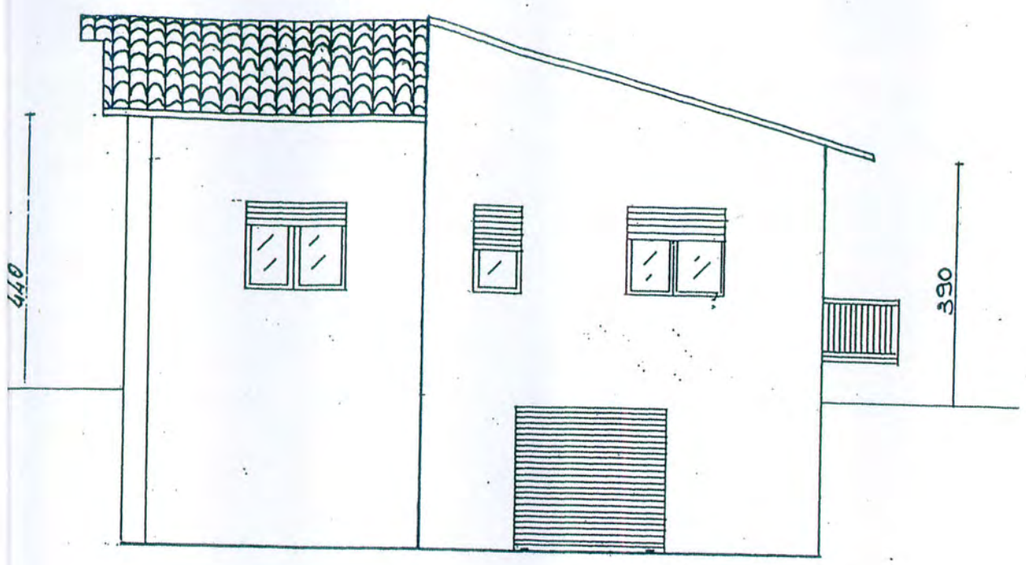

PROSPETTO LATERALE Dx

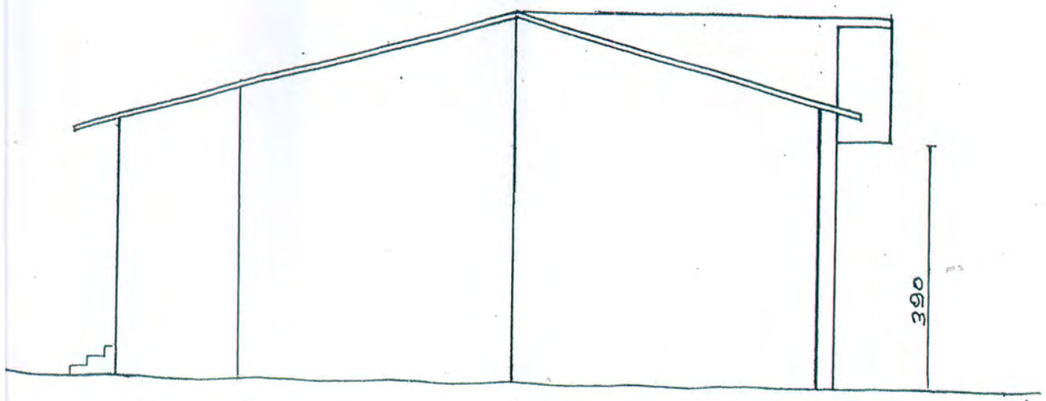

scala 1:100

grafici Progetto a Sanatoria

calcolo Hm = (6.25+6.35)/2 = mt 6.30

PROSPETTO LATO POSTERIORE

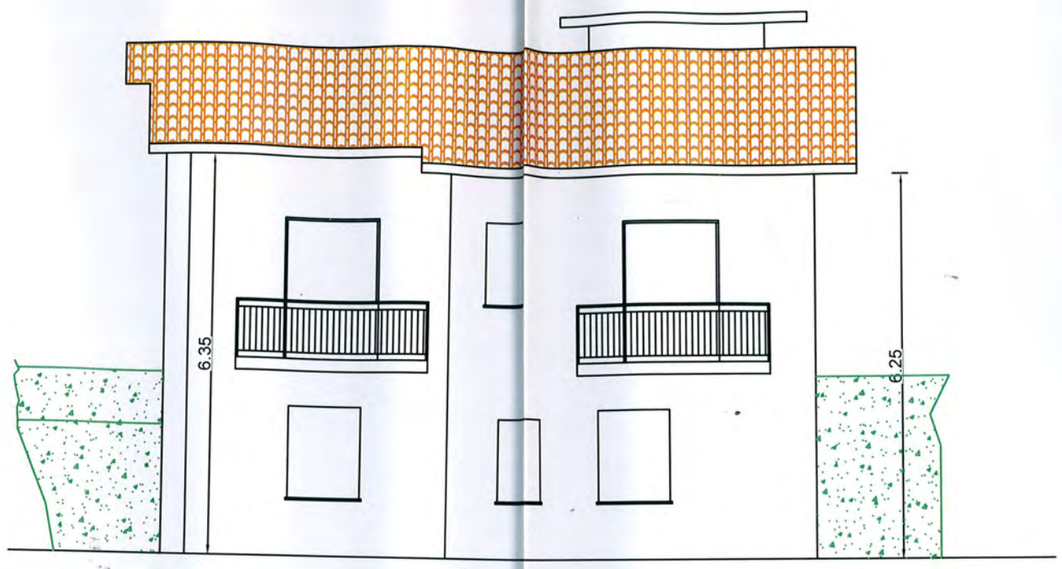

calcolo Hm = (6.35+3.85)/2 = mt 5.10

PROSPETTO LATERALE DX

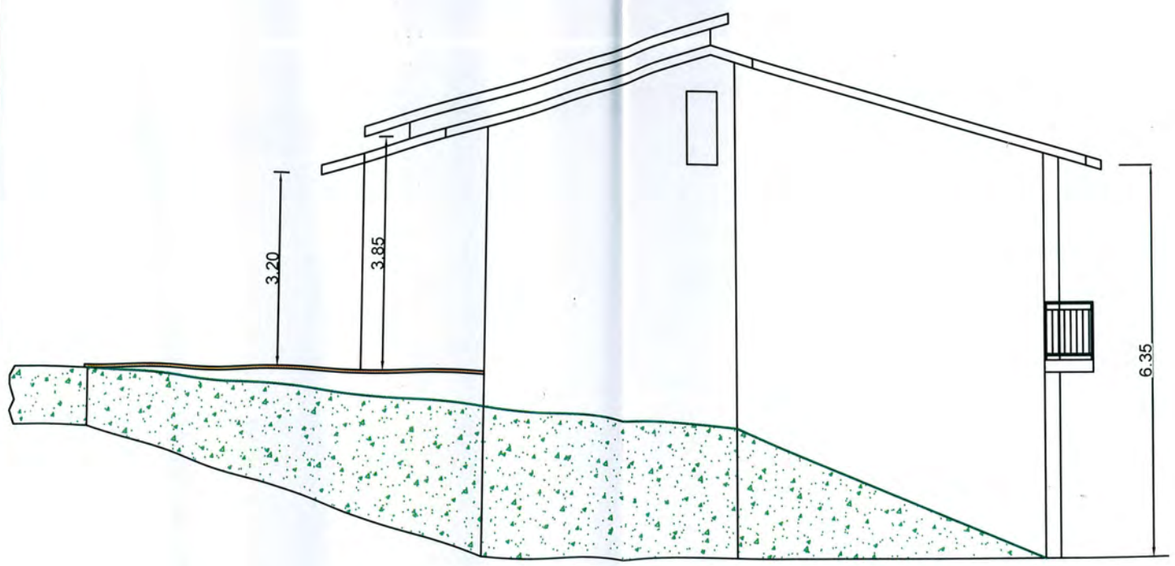

scala 1:100